


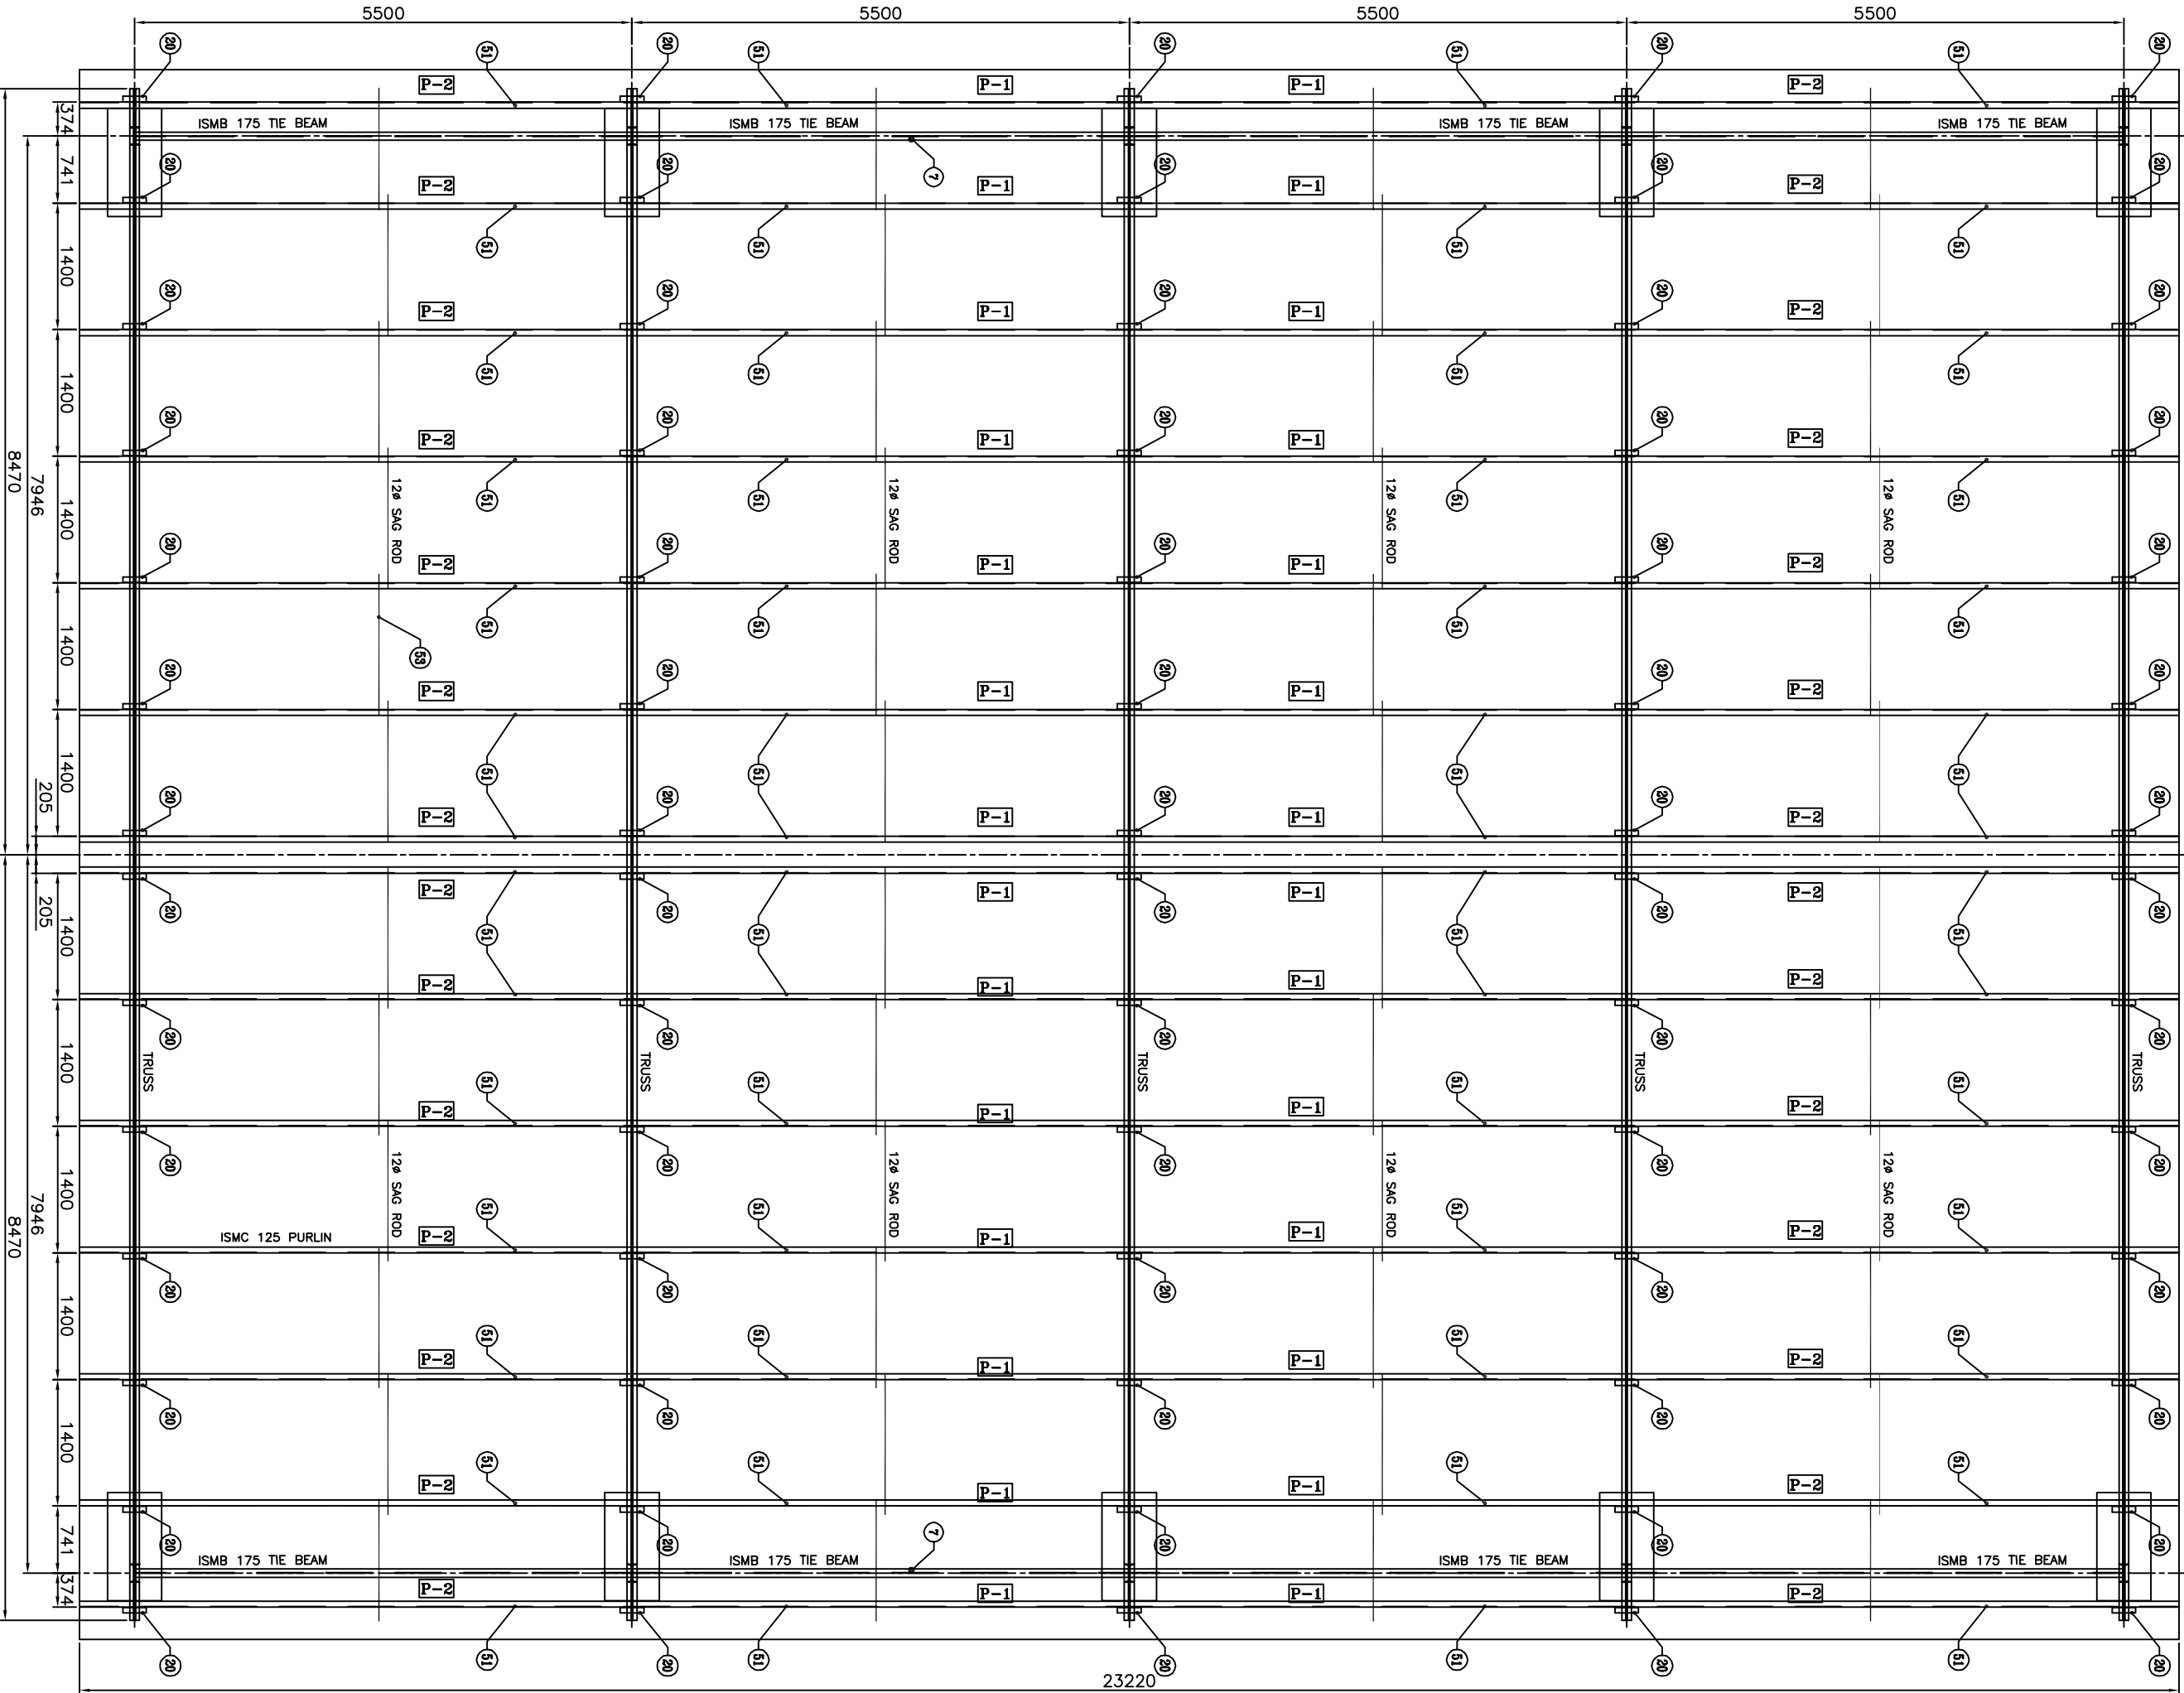
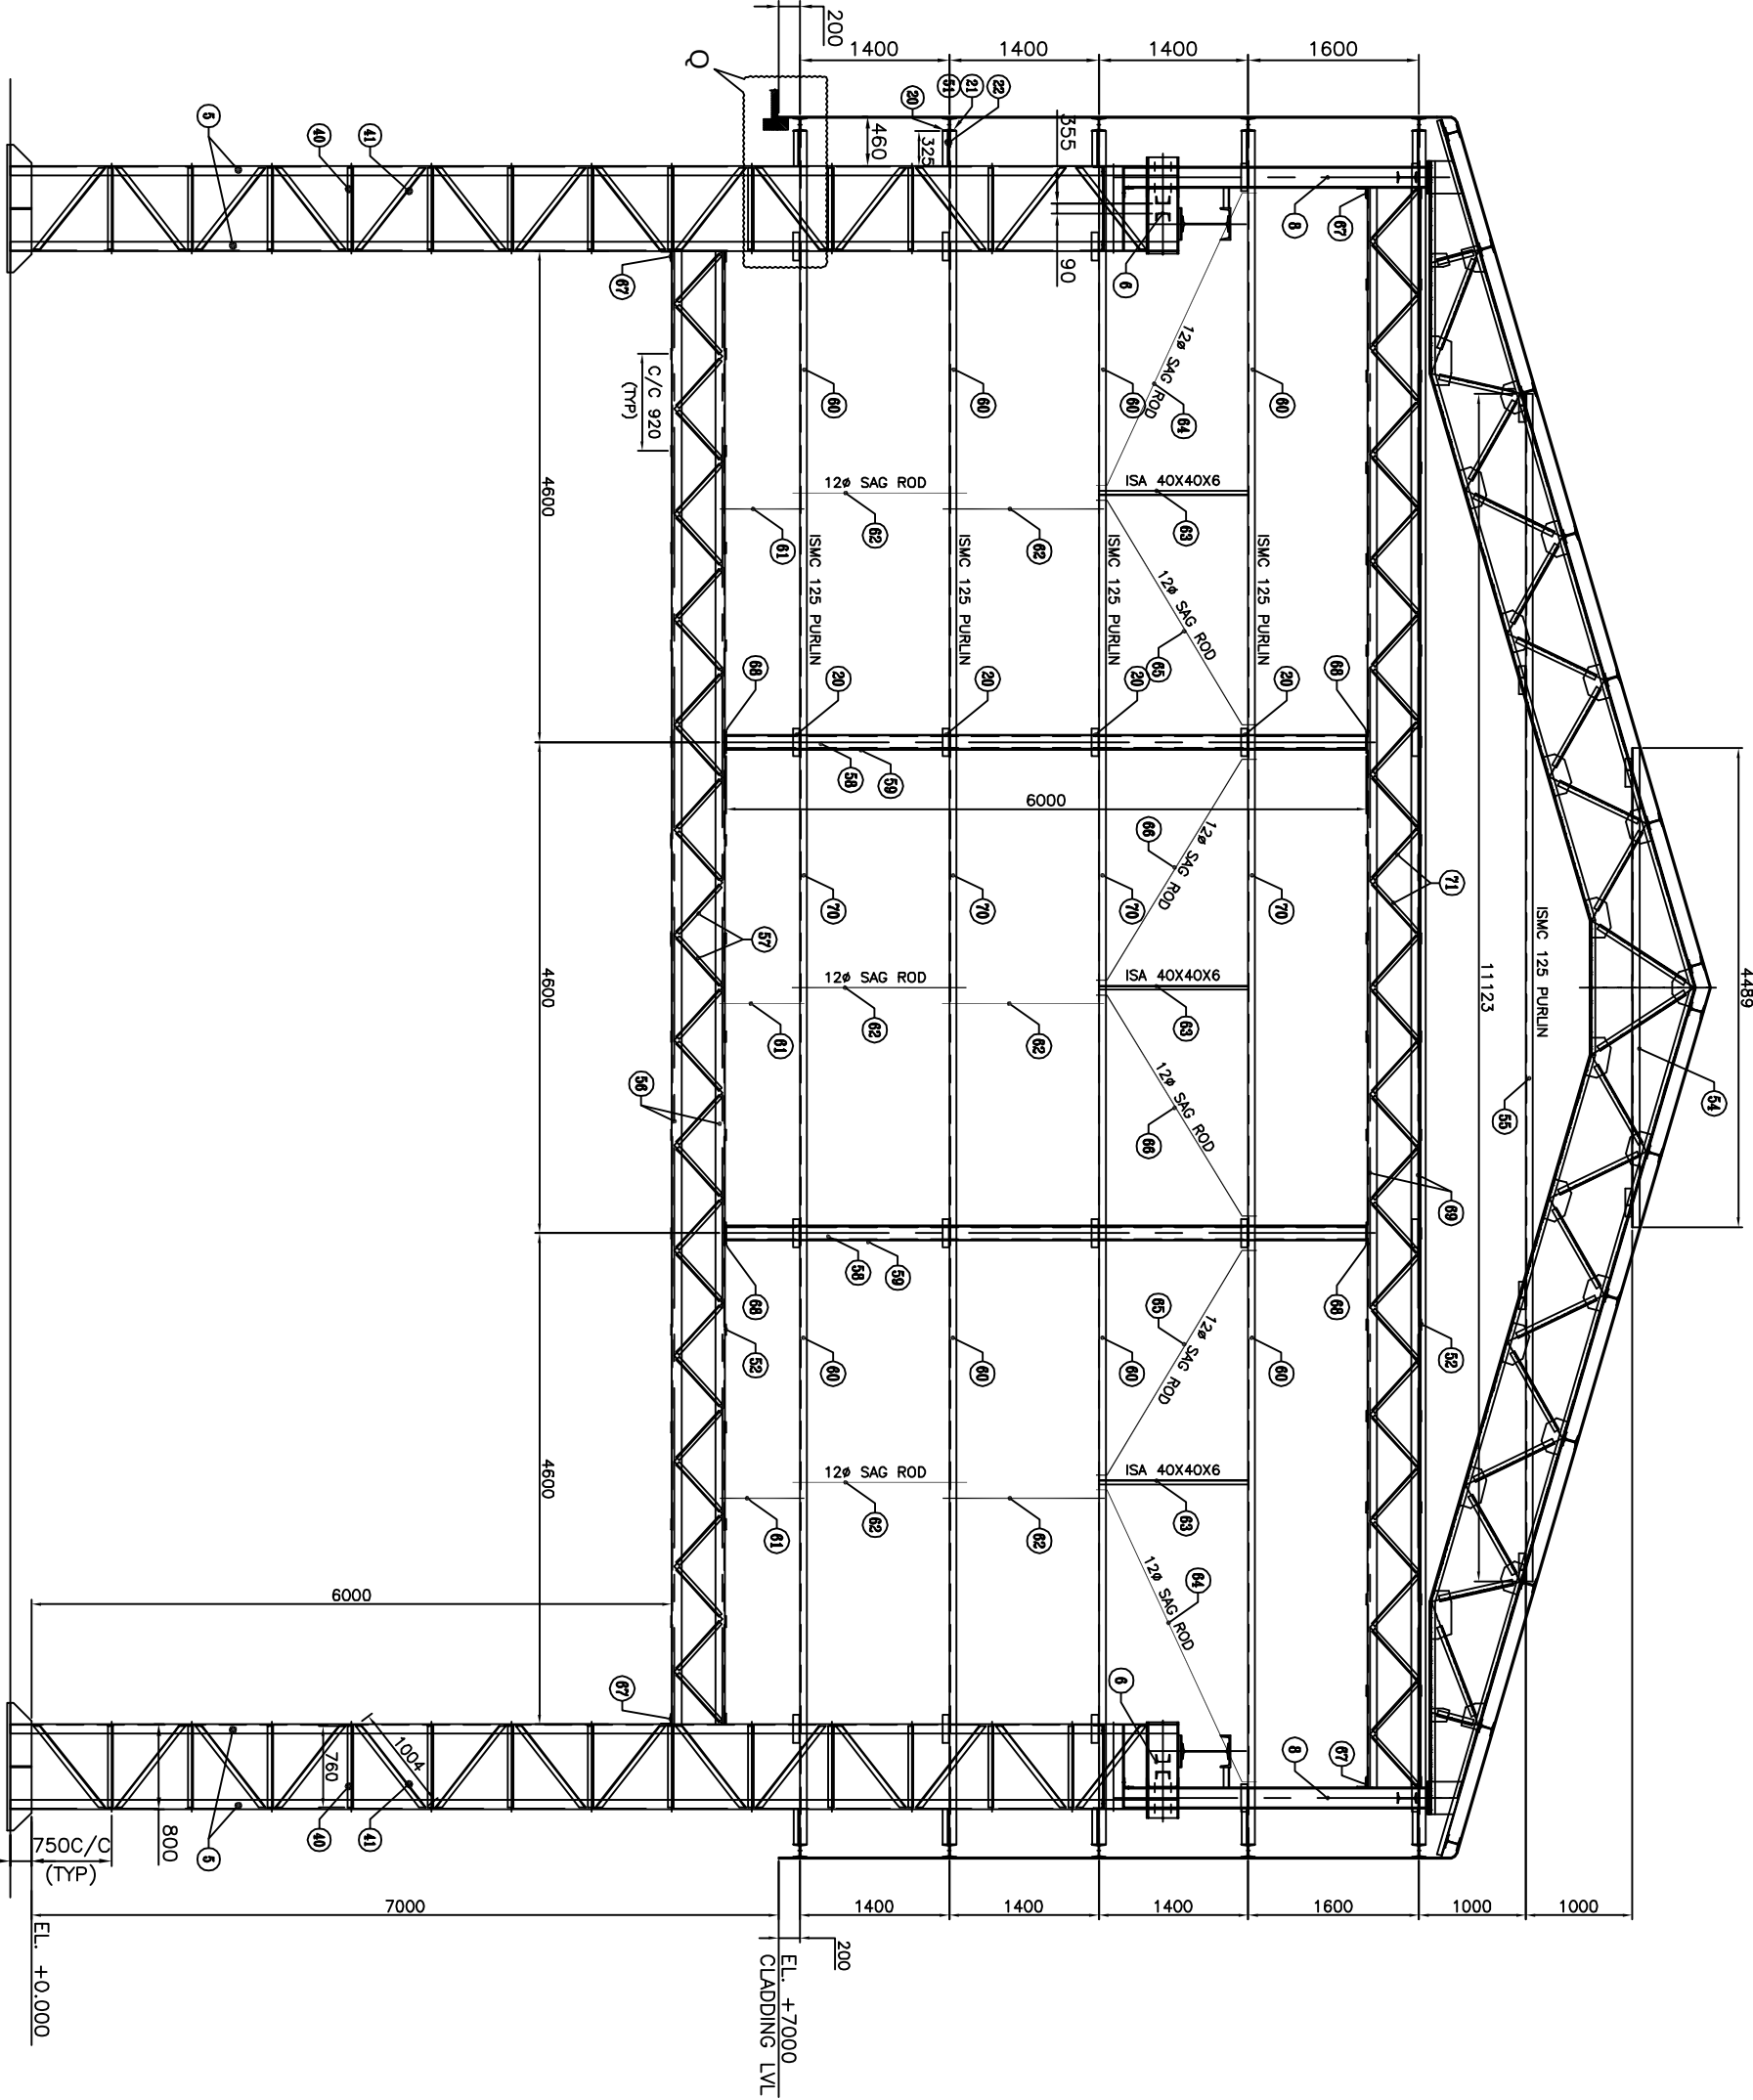


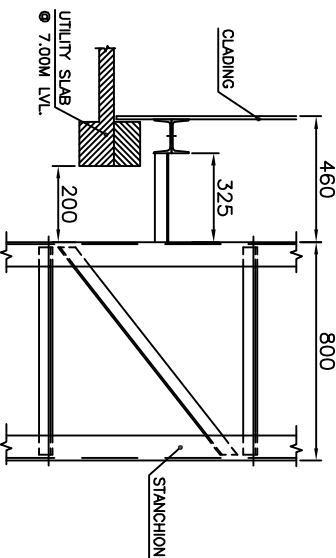

ROOF PLAN AT PURLING LEVEL

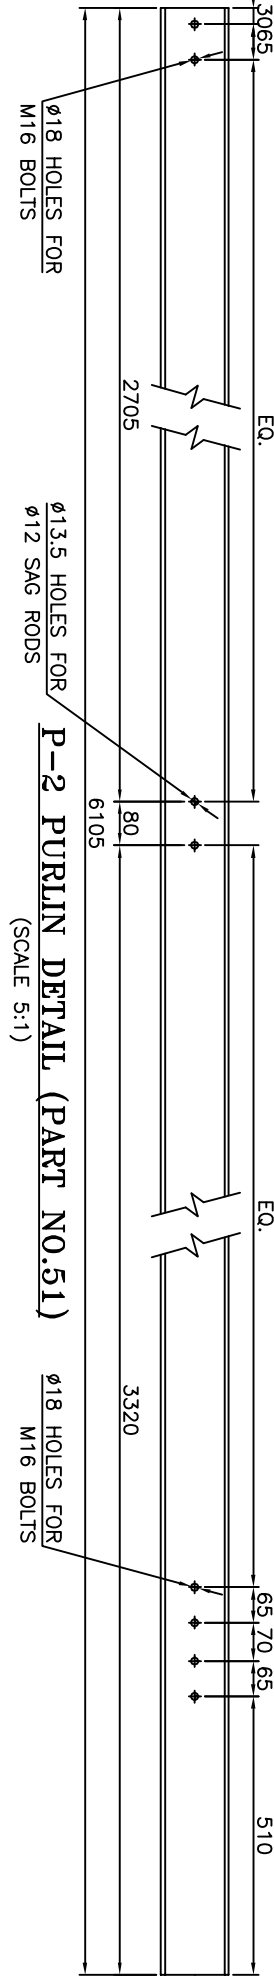

CLADDING ELEVATION FOR STRL. SHED

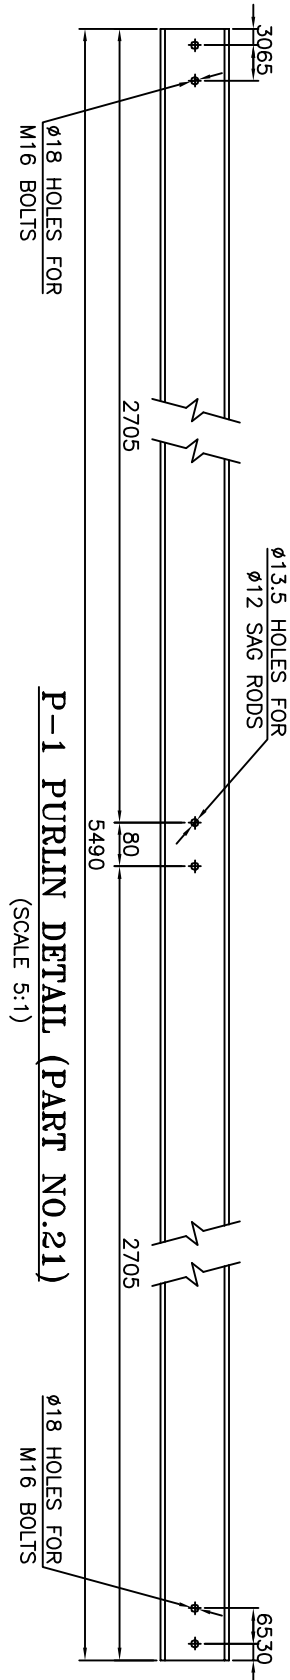

DETAIL-Q
(SCALE 2.5:1)